


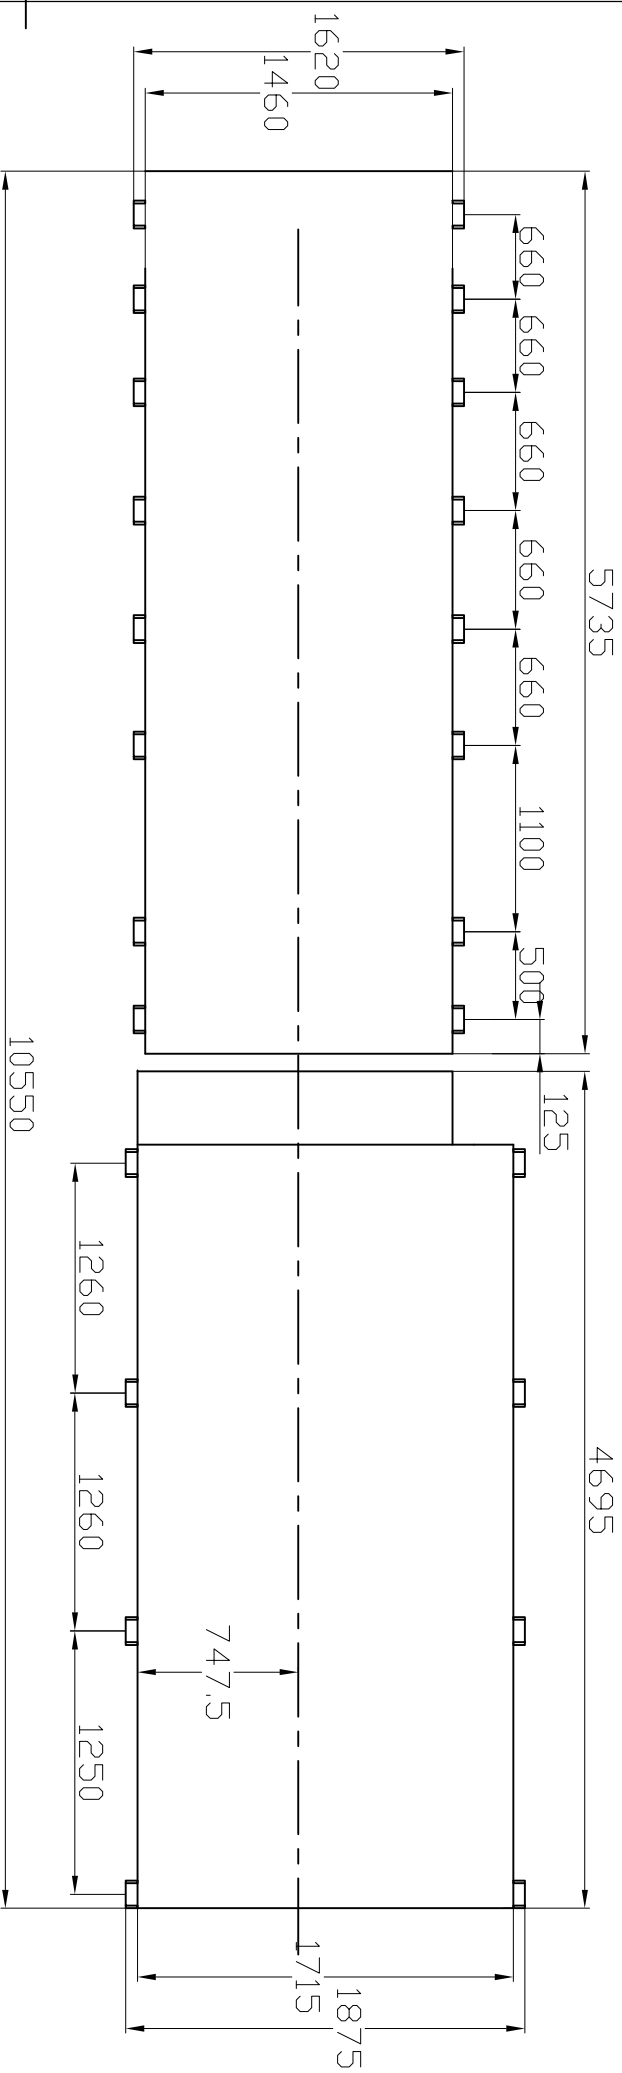

U1080TS地基示意图

1. 地基深1.2m, 平均每0.4m铺一根的钢筋, 分三层, 地坪水平打平, 每个垫脚下铺10mm厚的铁板铺地平面上。
2. 要求地面承载强度应大于10T/m
3. 机器必须接地。

3. 机器必须接地。

3. 机器必须接地。

地平面

钢筋水泥

1200

										地基示意图	
		分区	更改文件号	年 月 日						U1080TS	
设计								重量	件/台		比例
校对											
审核									1		
工艺			批准					版本			