



A

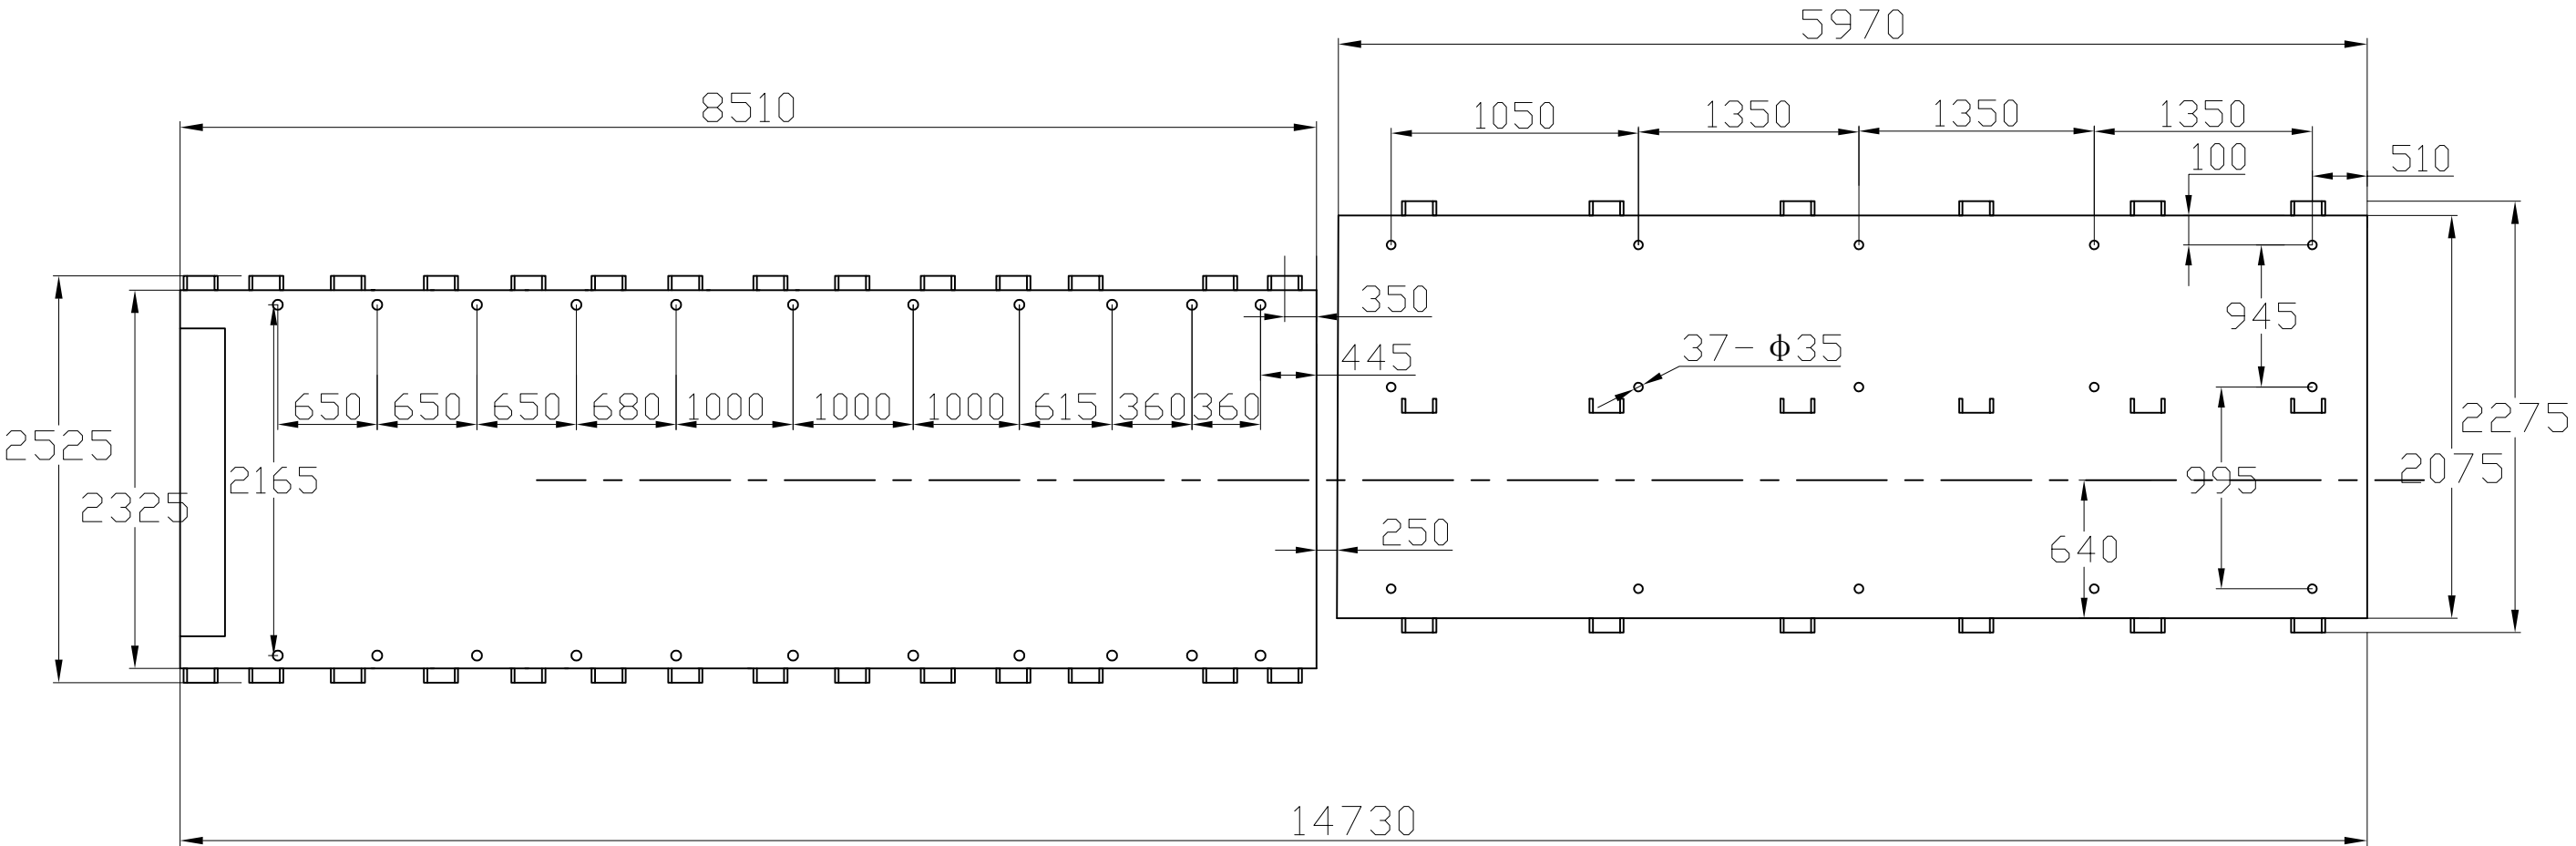

B

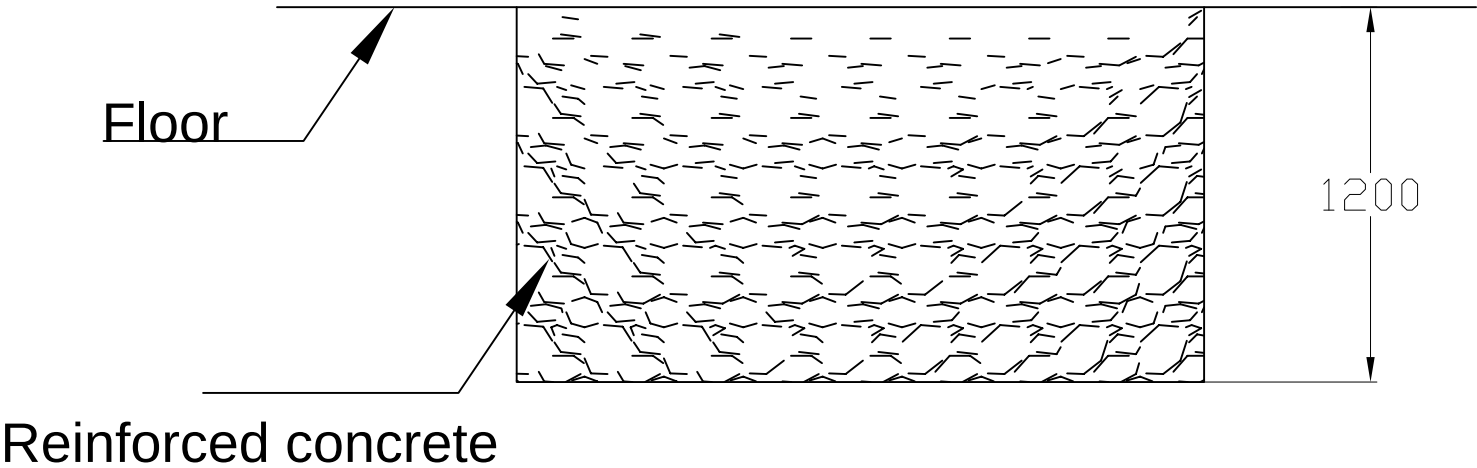

U2000TS Foundation Drawing

1. The foundation is 1.2m deep. D16 steel bars are laid every 0.4m in three layers. The ground is leveled and a 10mm thick iron plate is placed under each footrest.
2. The ground bearing strength must be greater than 10t/m.
3. The machine must be grounded.
4. Leave space for a 2m high-pressure oil pipe on the left side of the machine and a 0.5m cooler on the right side.

描校

日期

		分区	更改文件号	年月日		重量	件/台	比例	地基示意图	
设计										
校对							1		U1900TS-00	
审核										
工艺			批准		版本					