


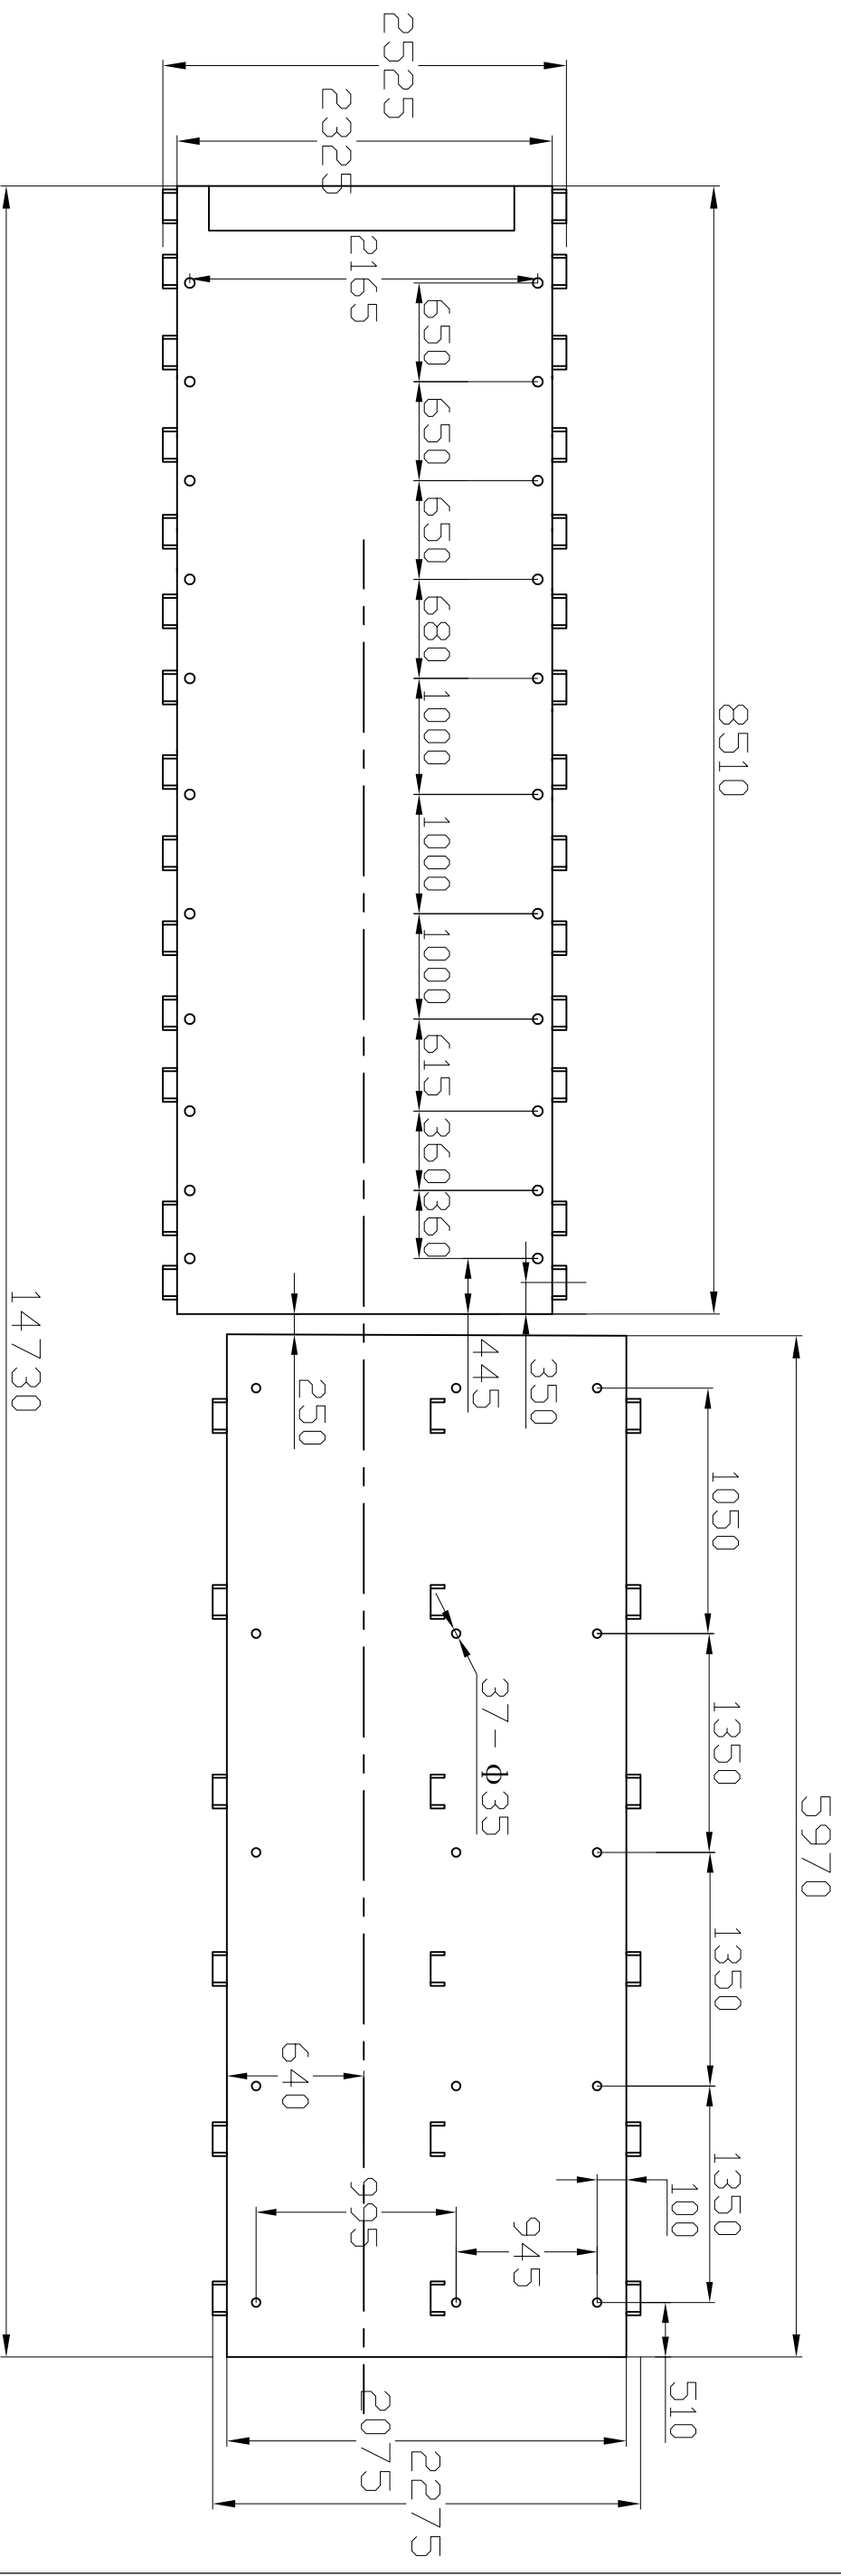

U2000TS地基示意图

1. 地基深1.2m, 平均每0.4m铺D16一根的钢筋, 分三层, 地坪水平打平, 每个垫脚下铺10mm厚的铁板铺地平面上。
2. 要求地面承载强度应大于10T/m
3. 机器必须接地。
4. 机器左边留2米高压油管位置, 右边留0.5米冷却器位置。

[illegible]