
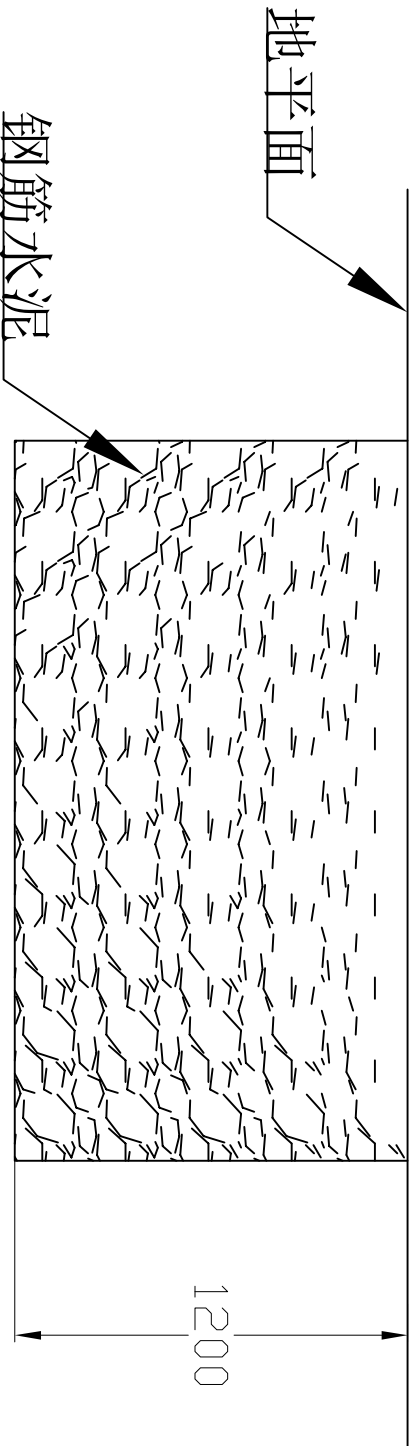


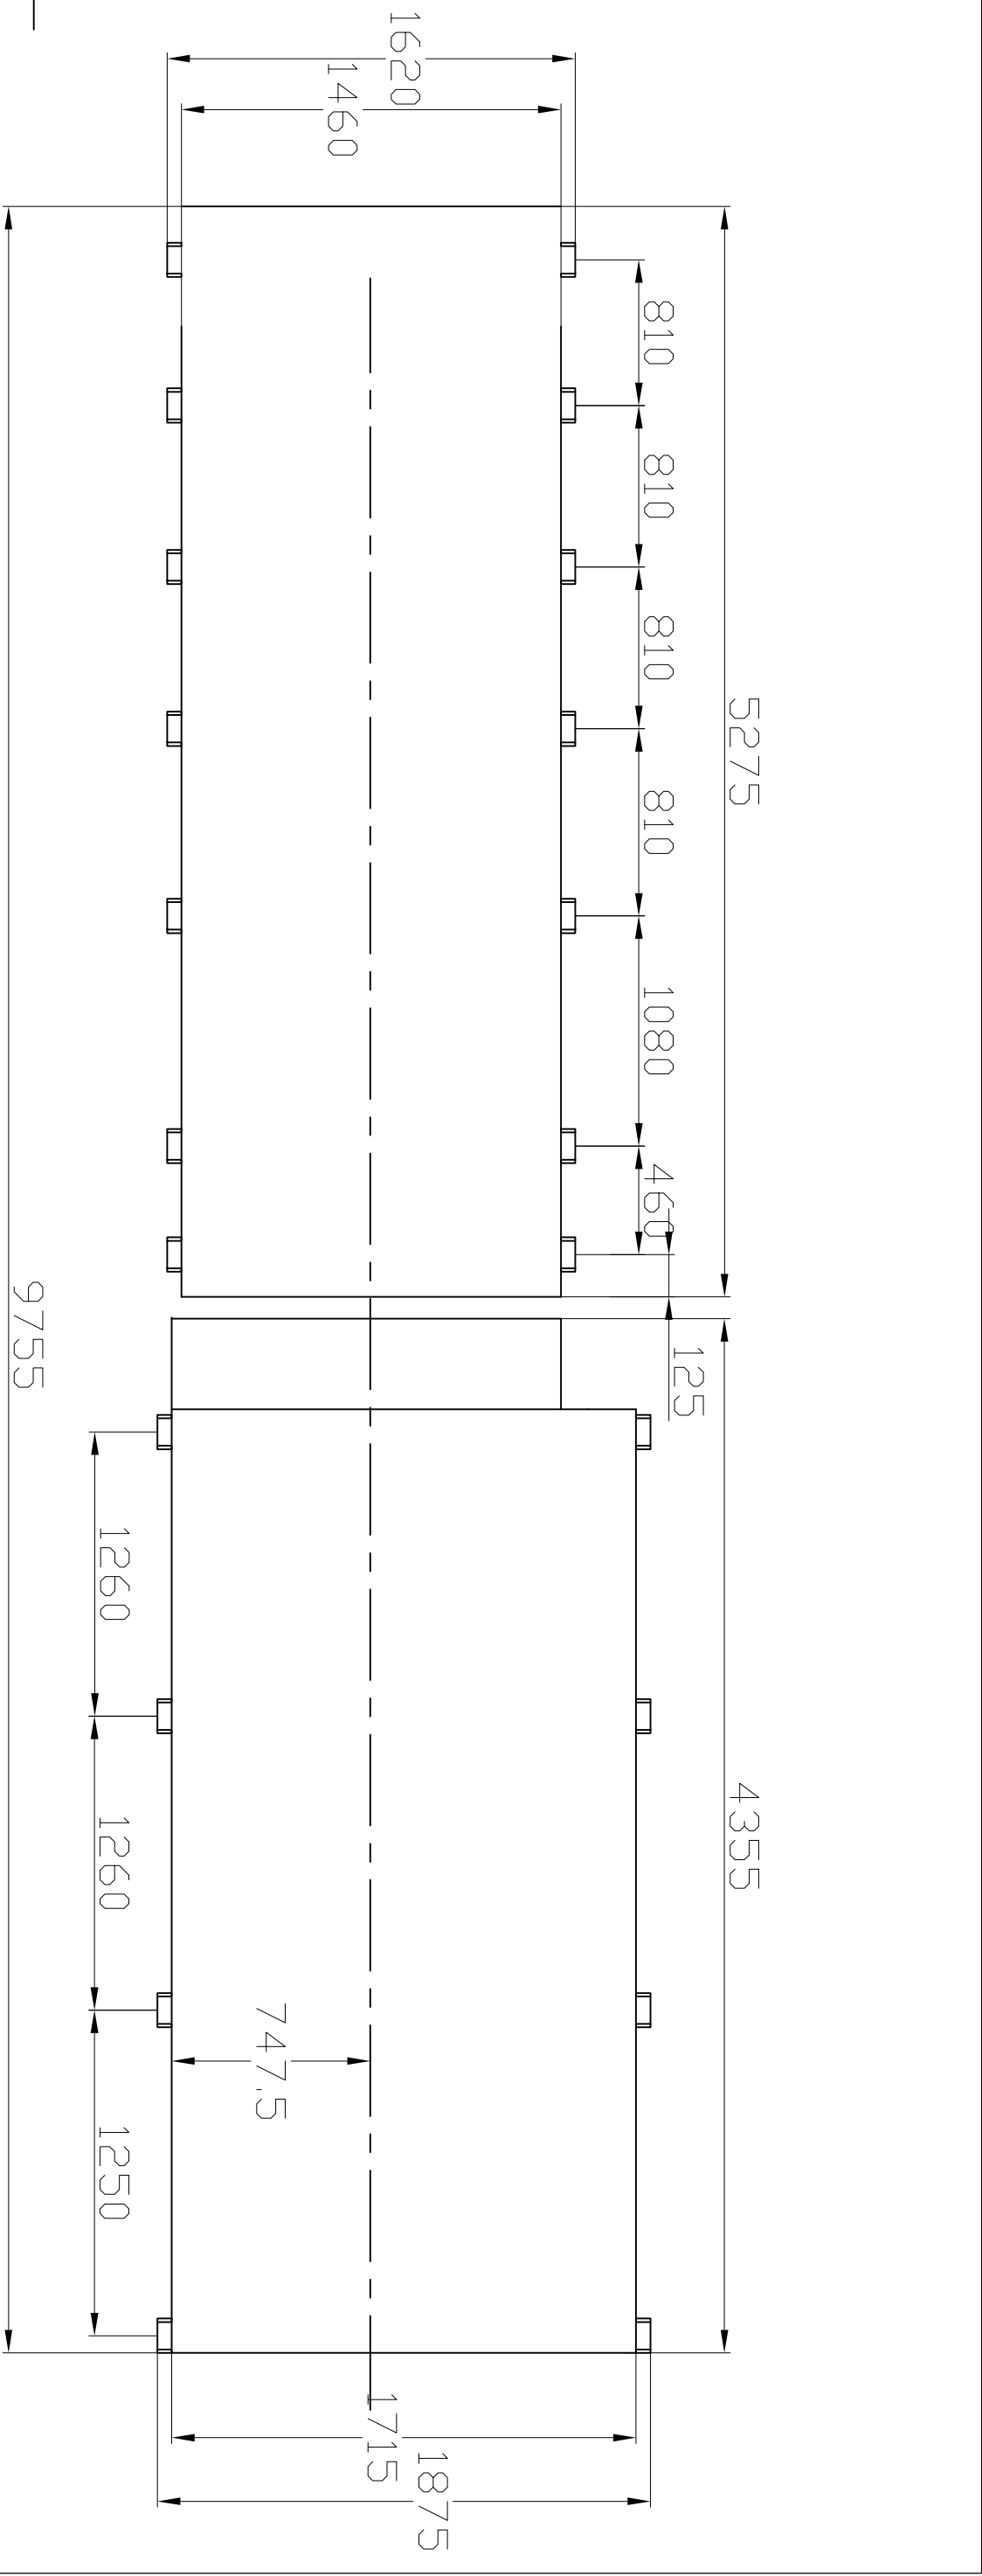

U800TS地基示意图
1. 地基深1.2m，平均每0.4m铺一根的钢筋，分三层，地坪水平打平，每个垫脚下铺10mm厚的铁板铺地平面上。
2. 要求地面承载强度应大于10T/m
3. 机器必须接地。

描校	
----	--	--	