


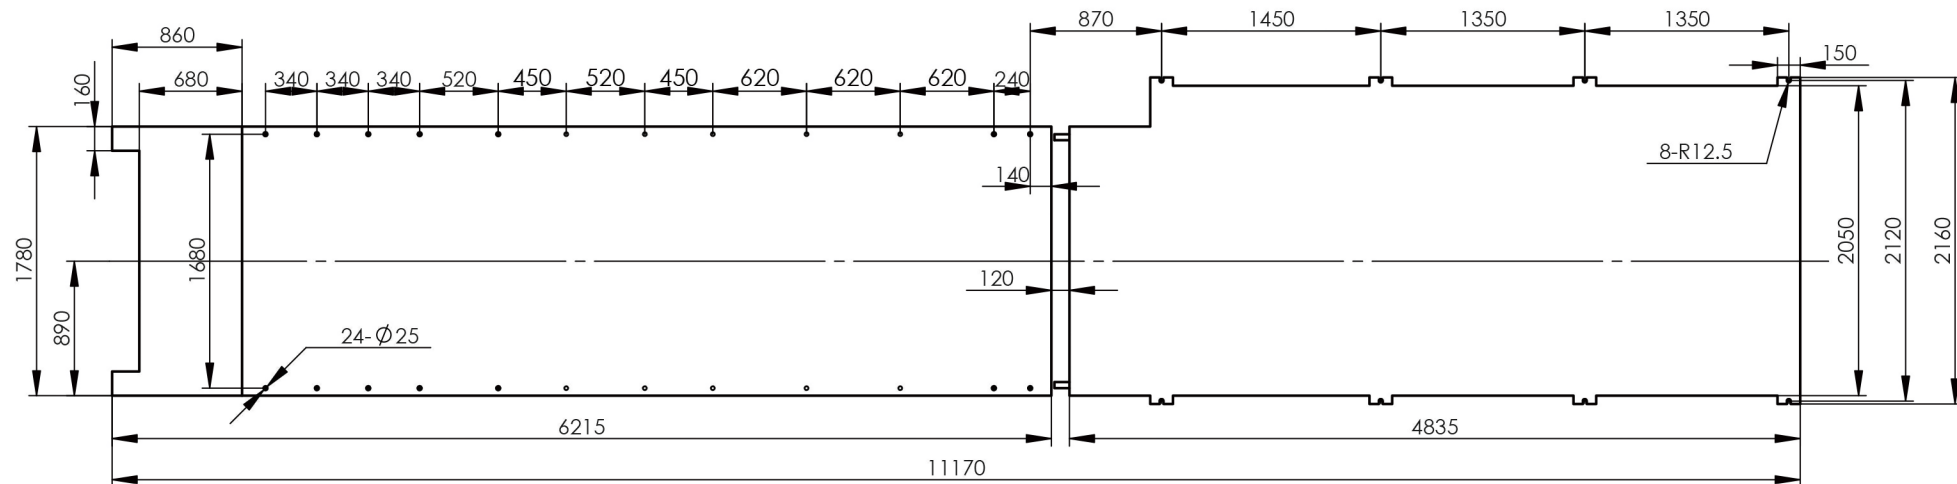

U1080TS Machine Frame

1. Foundation depth should be 1.2m and divided into three layers by three D16 mm rebar in each 0.4m depth.
2. Planish the ground horizontally and put a 10mm iron plate under each machine frame pad.
3. Foundation ground bearing capacity should larger than 10T/m.
4. Machine must connected with earth wire.
5. This is just a foundation drawing, please refer outside dimension to real machine.

